জিলা খুলনা

থানা খুলনা

মৌজা | হেলাতলা ও সিটনং ৩

রেভেনিউ সার্ভে নং ৩৯৯৭

স্কেল ৩২" = ১ মাইল

খুলনা মিউনিসিপ্যালিটি ভুক্ত

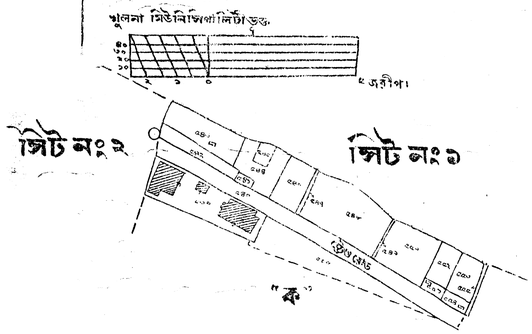

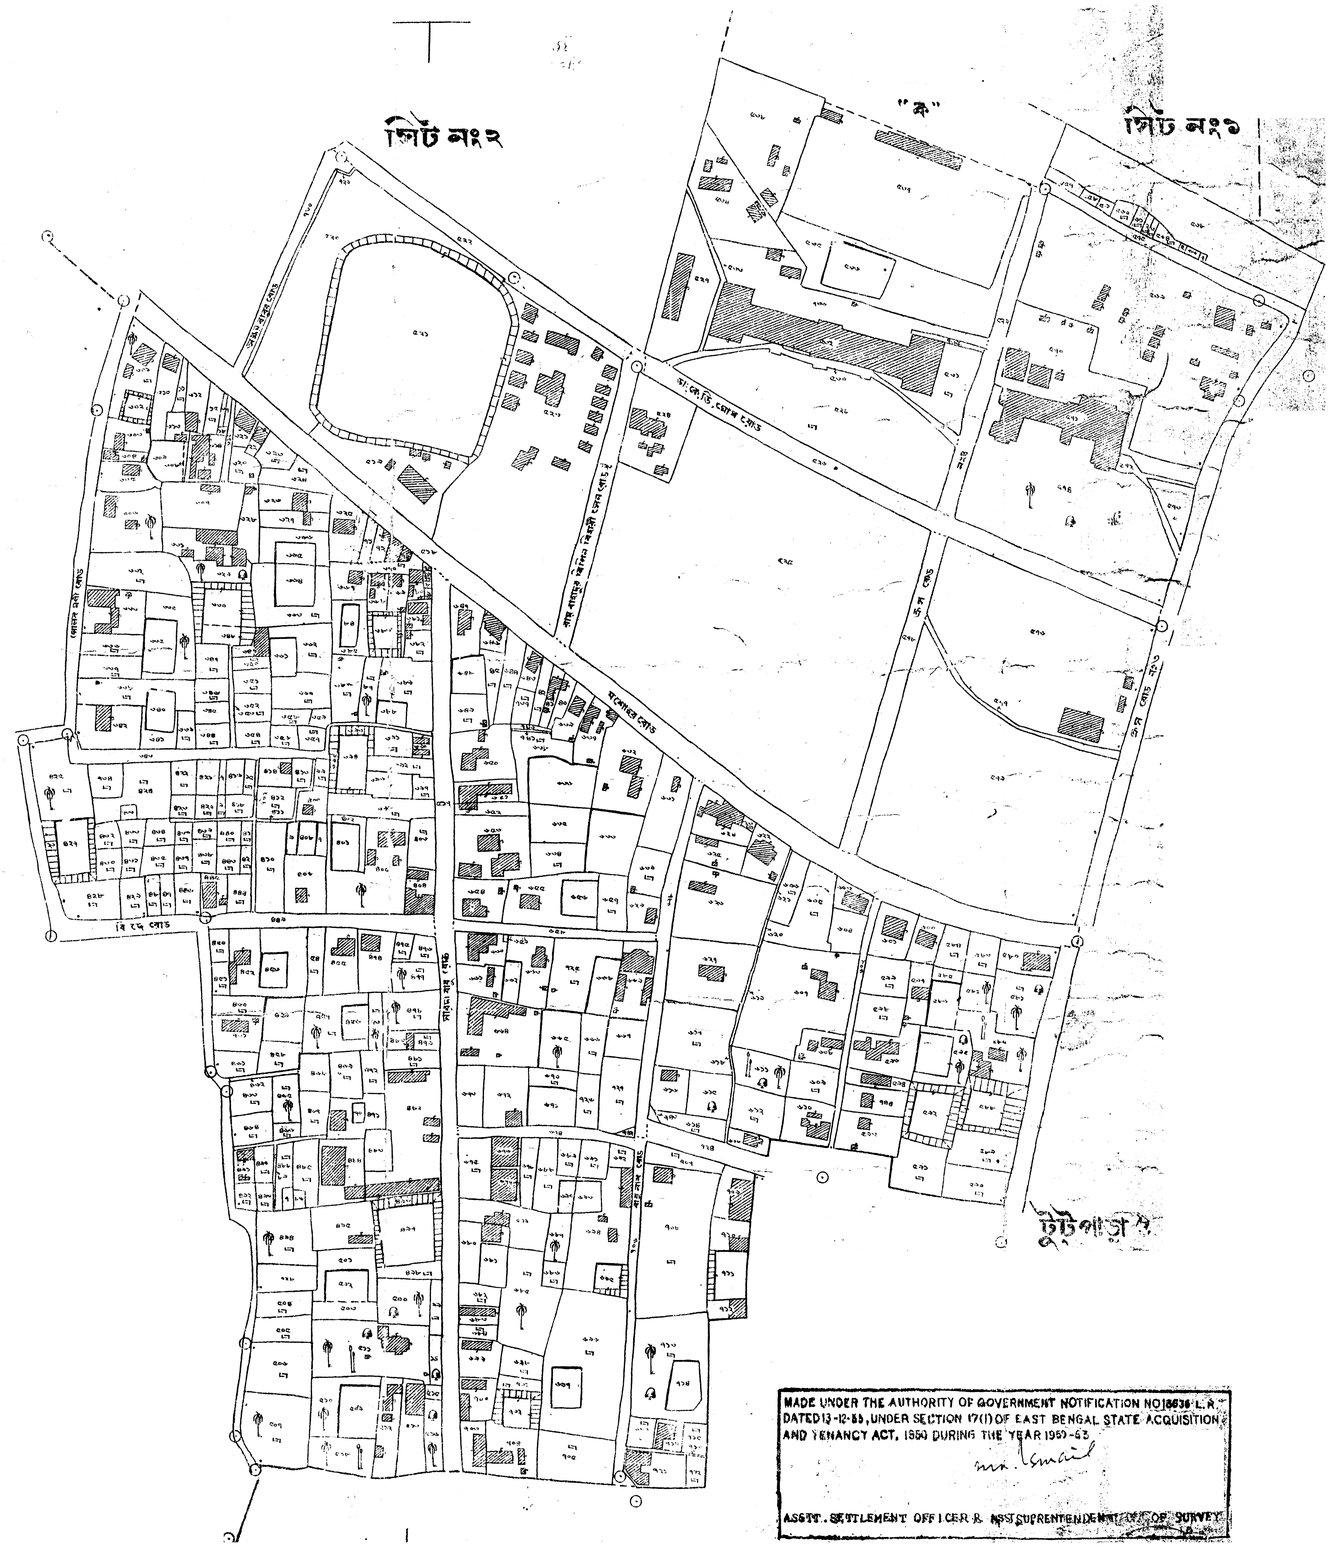

সাঙ্কেতিক

শালান	⊔
ত্রিশীমানার পিলার	A
অন্যান্য পিলার	⊡
ষ্টেসন (ট্রাভার্স)	⊙

দাগ নং

হলট ·· ×

রাস্তা ·· ৩৪৩, ৩৪৮, ৩৪৯, ৩১৭, ৩২২, ৩২৩, ৩৪১, ৩২৬, ৩২৪, ৩২৩, ৭২৪

খাল ·· ×

অত্র সিটে ভুক্ত ·· ৩৩১ – ৭২১, ৭২৩ – ৭৩৭, ৭৪০ – ৭৪৪

MADE UNDER THE AUTHORITY OF GOVERNMENT NOTIFICATION NO 18636 L.R. DATED 13-12-55, UNDER SECTION 17(1) OF EAST BENGAL STATE ACQUISITION AND TENANCY ACT, 1950 DURING THE YEAR 1960-63

ASSTT. SETTLEMENT OFFICER & ASST SUPRENTENDENT OF SURVEY