
থানা দৌলতপুর মৌজা বয়রা জে, এল, নং- ১০ সিট লং- ৪

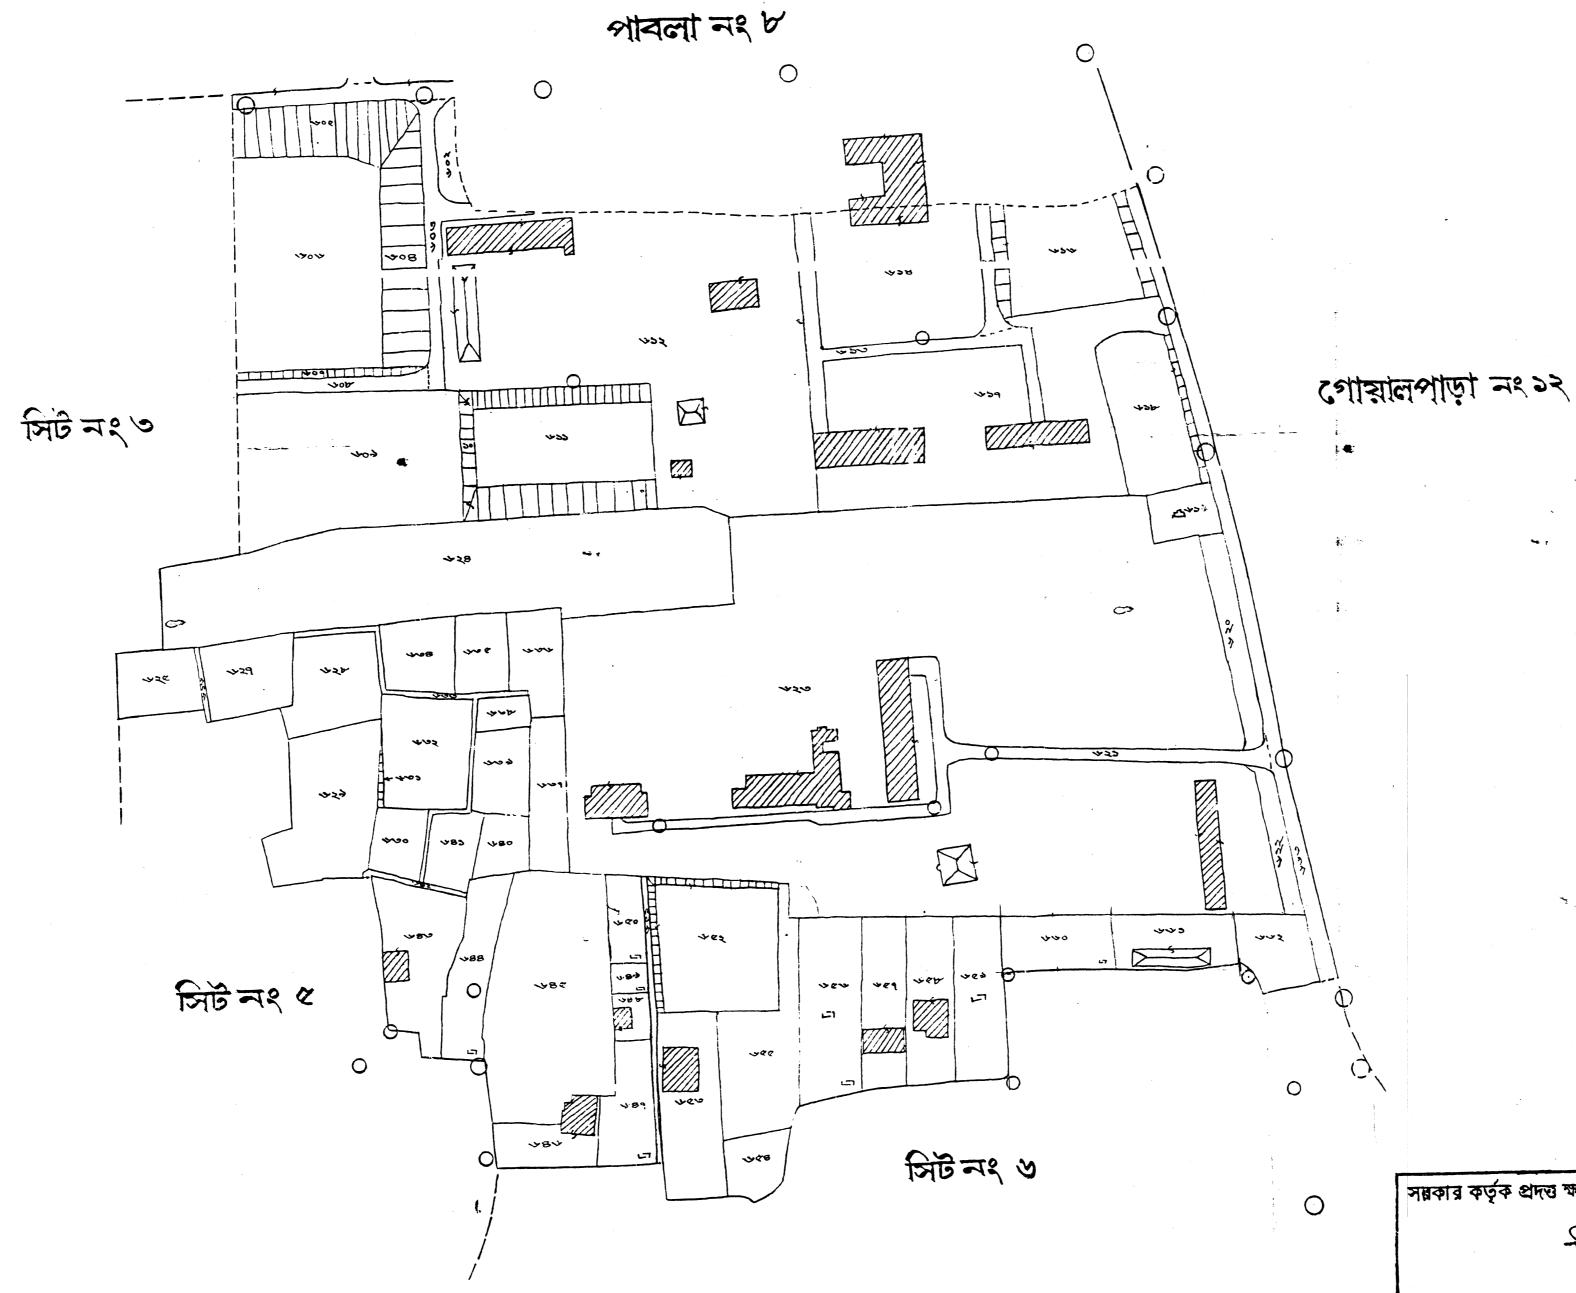





| সাঞ্চেক   |                   |                |                               |
|---|-------------------|----------------|-------------------------------|
| দালান   | ***               |                |                               |
| ত্রিসীমানার পিলার                                       | ***               | 100            | A                             |
| লোহার পিলার   | •••               | ***            | 1                             |
| জনান্য পিলার  | • •••             | ***            | <u> </u>                      |
| ট্রাভার্স ষ্টেশন নতুন                                   | •••               | •••            | 0                             |
| ট্রাভার্স ষ্টেশন পুরাতন                                 | to.               | •••            | . O                           |
| জি, টি, ষ্টেশন  | ,,,               | •••            |                               |
| বেশ্বমার্ক  | ***               | <b>\</b>       | <del>û</del>                  |
| ইন্দারা   | •••               | ***            | <b>®</b>                      |
| নলকৃপ   | •••               | •••            | <b>(4)</b>                    |
| পানবরজ  | 444               | •••            |                               |
| 111144  |                   |                | 2.0                           |
| मांश्र नश   |                   |                |                               |
| পাকা রাস্তা <u>২০২ খু</u><br>কাঁচা রাম্ভা স<br>খাল খুং৪ | 0 <b>'0', '</b> ' | - K3'<br>- K3' | ) x , w , y , w , w , w , w , |
| অত্র সিটভৃষ্ণ ৩০২-১                                     | <b>ઝ</b> ુ જ      | ٠,             |                               |
| বাটা দাপ ×  |                   |                |                               |
|   |                   |                | and the same                  |

সম্বকার কর্তৃক প্রদন্ত ক্ষমতাবলে ২ ১ ১৬ -২০০০ সনে প্রস্তুত निर्मल ठन्म उपरंकारा

সেটেলমেন্ট অফিসার এবং সুপারিনটেনডেন্ট অব সার্ভে